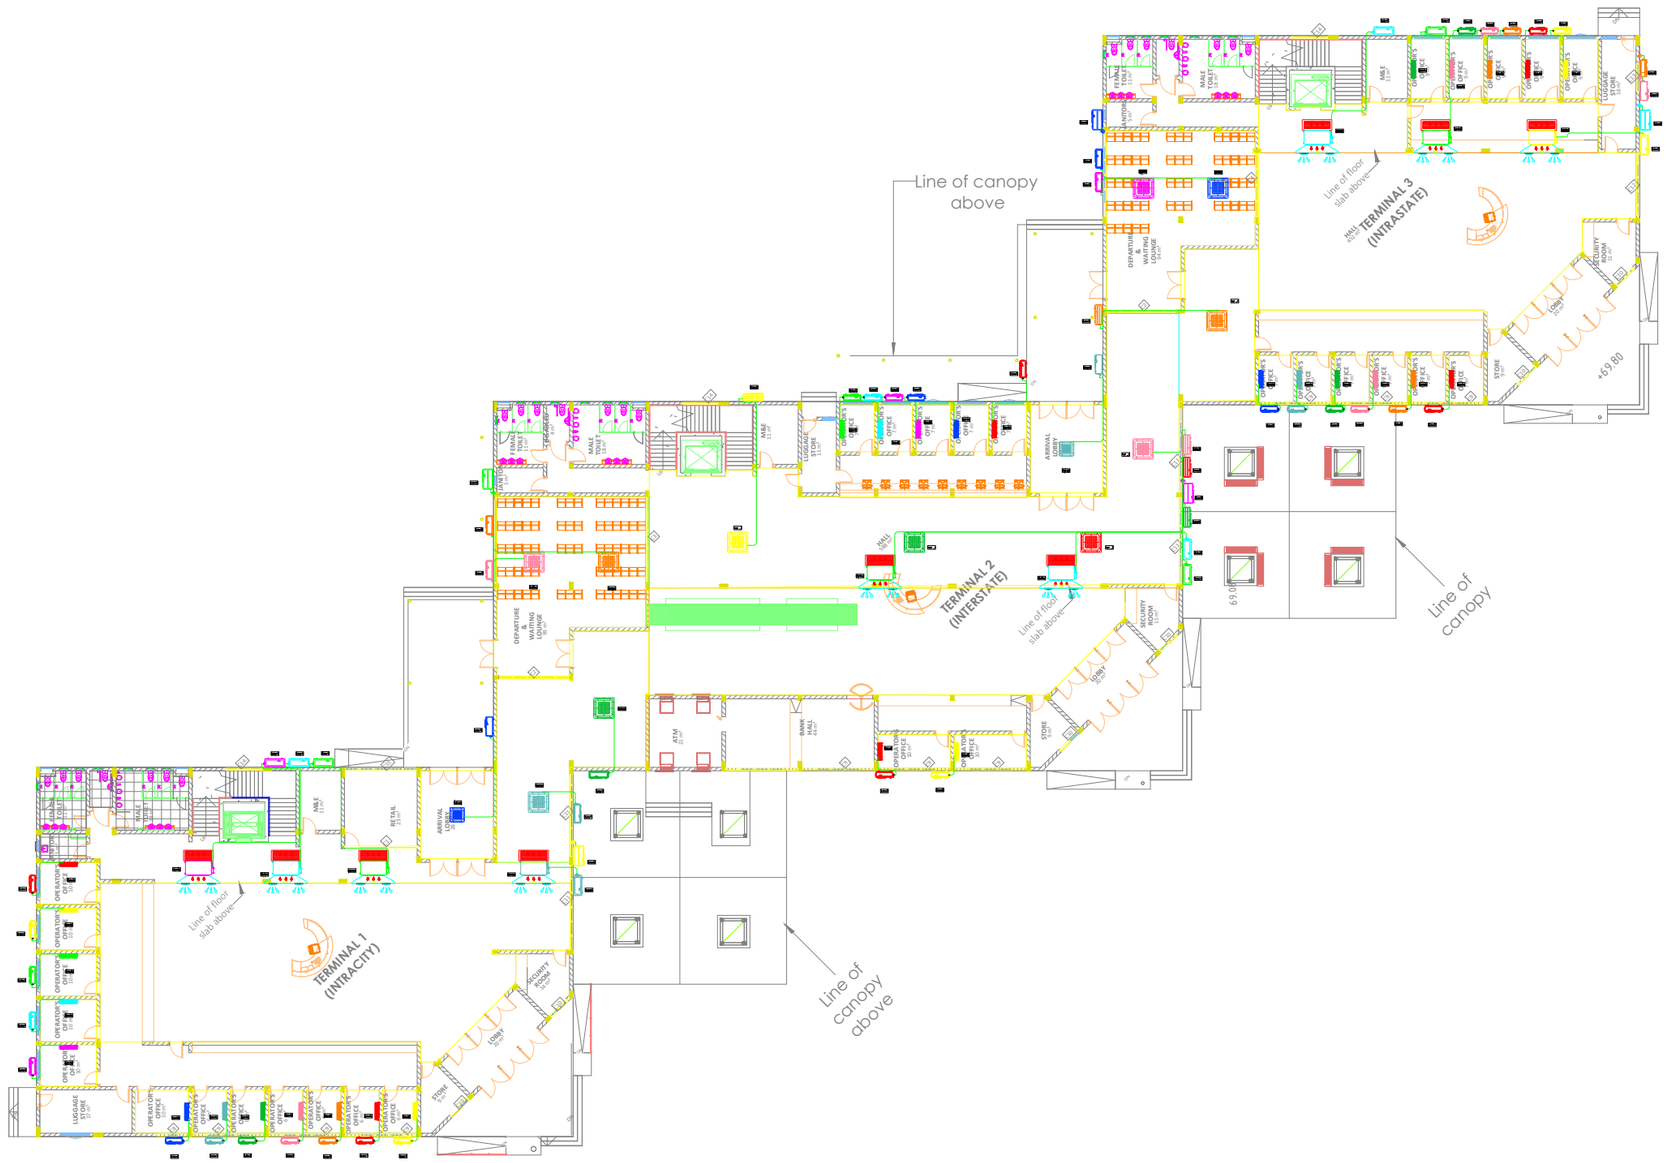


NOTE

PROJECT TITLE

PROPOSED HVAC DESIGN FOR ASSUMPTA BUS TERMINAL

DRAWN KOLAWOLE

CHECKED

APPROVED

DRAWING TITLE

ASSUMPTA TERMINAL

DRAWING NO.

GROUND FLOOR PLAN

DATE 30th JANUARY, 2026.

SCALE

SHEET NO.

REV. NO.