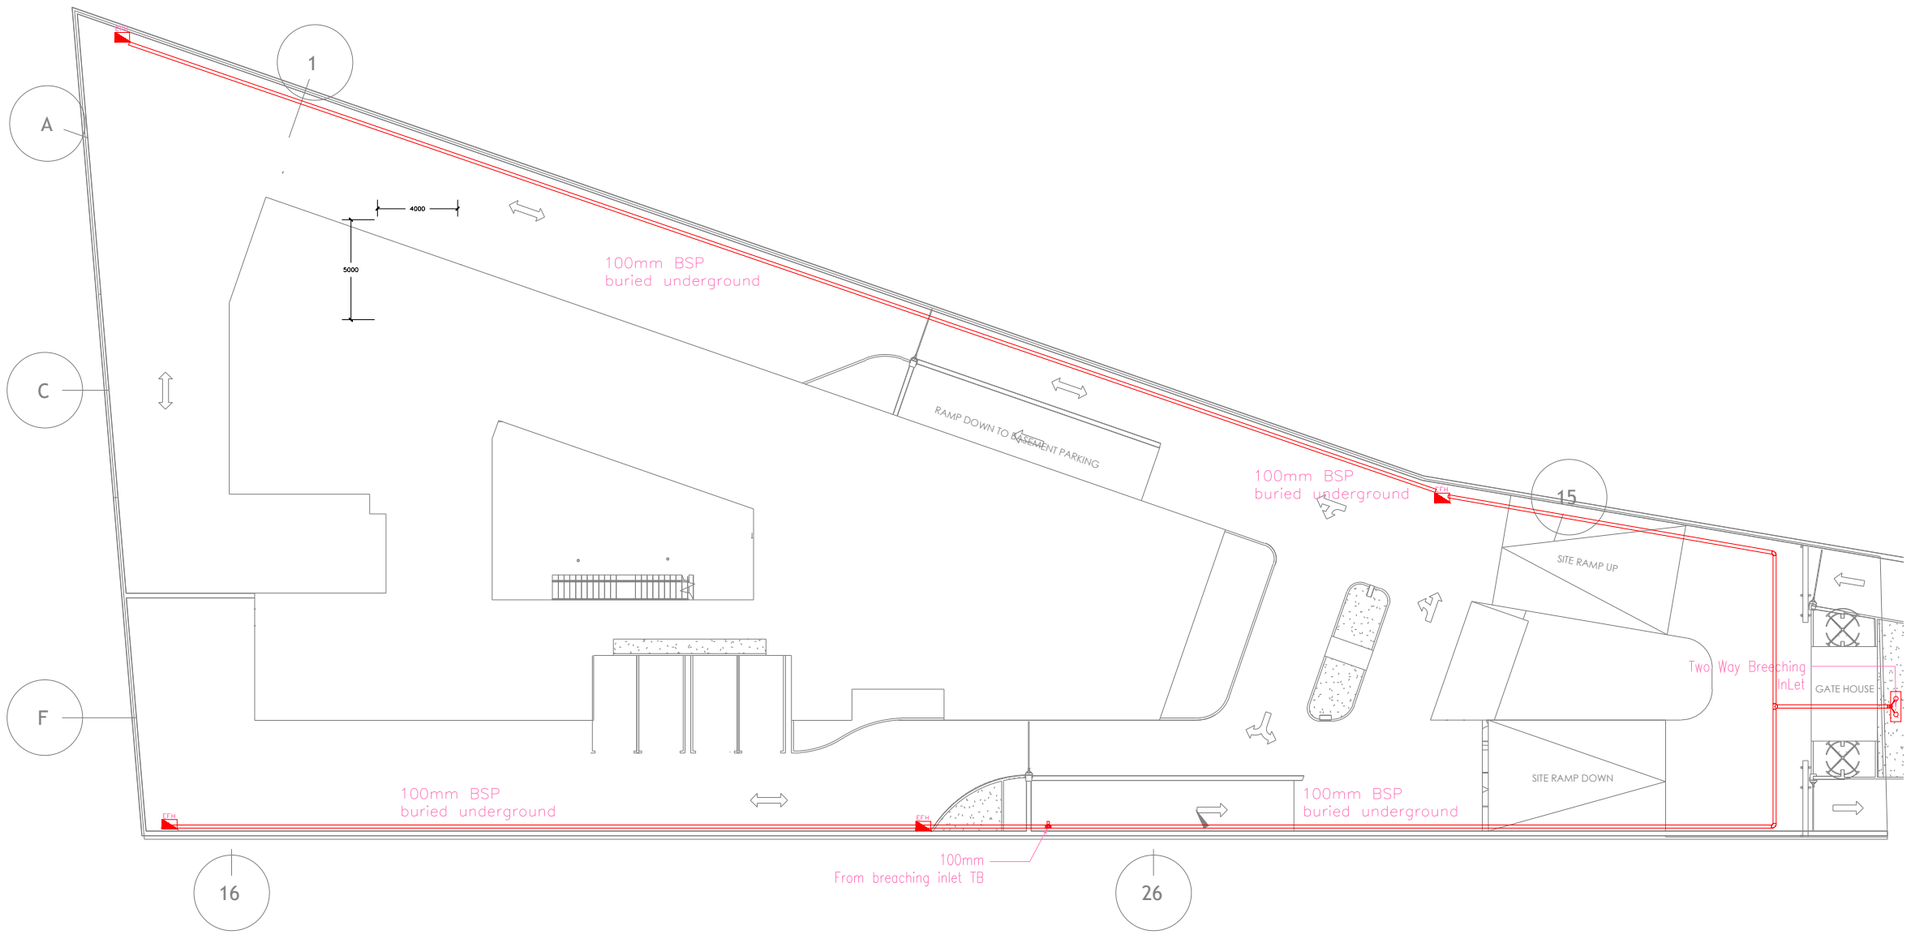


SITE PLAN

SITE PLAN
FIREFIGHTING LAYOUT.

NOTES

-Measurements should be taken from c/c dimensions to be read, not scaled.

-Given dimensions in metric mm.

-Architectural drawing to be read in conjunction with relevant structural drawing.

-Any alteration to be done with the approval of the project architect.

Architects

CLIENT

KING GEORGE HOTEL IKEJA.

PROJECT TITLE


PROPOSED KING GEORGE COURT LUXURY HOTEL DEVELOPMENT.

SHEET TITLE

SITE PLAN
FIREFIGHTING LAYOUT

		DATE
DESIGNED BY	A.K	MAY,2026..
CAD BY	A.H	MAY,2026..
CHECKED BY		MAY,2026..

SCALE REF NO.	SHEET NO.		DRAWING NO.
			DR-01

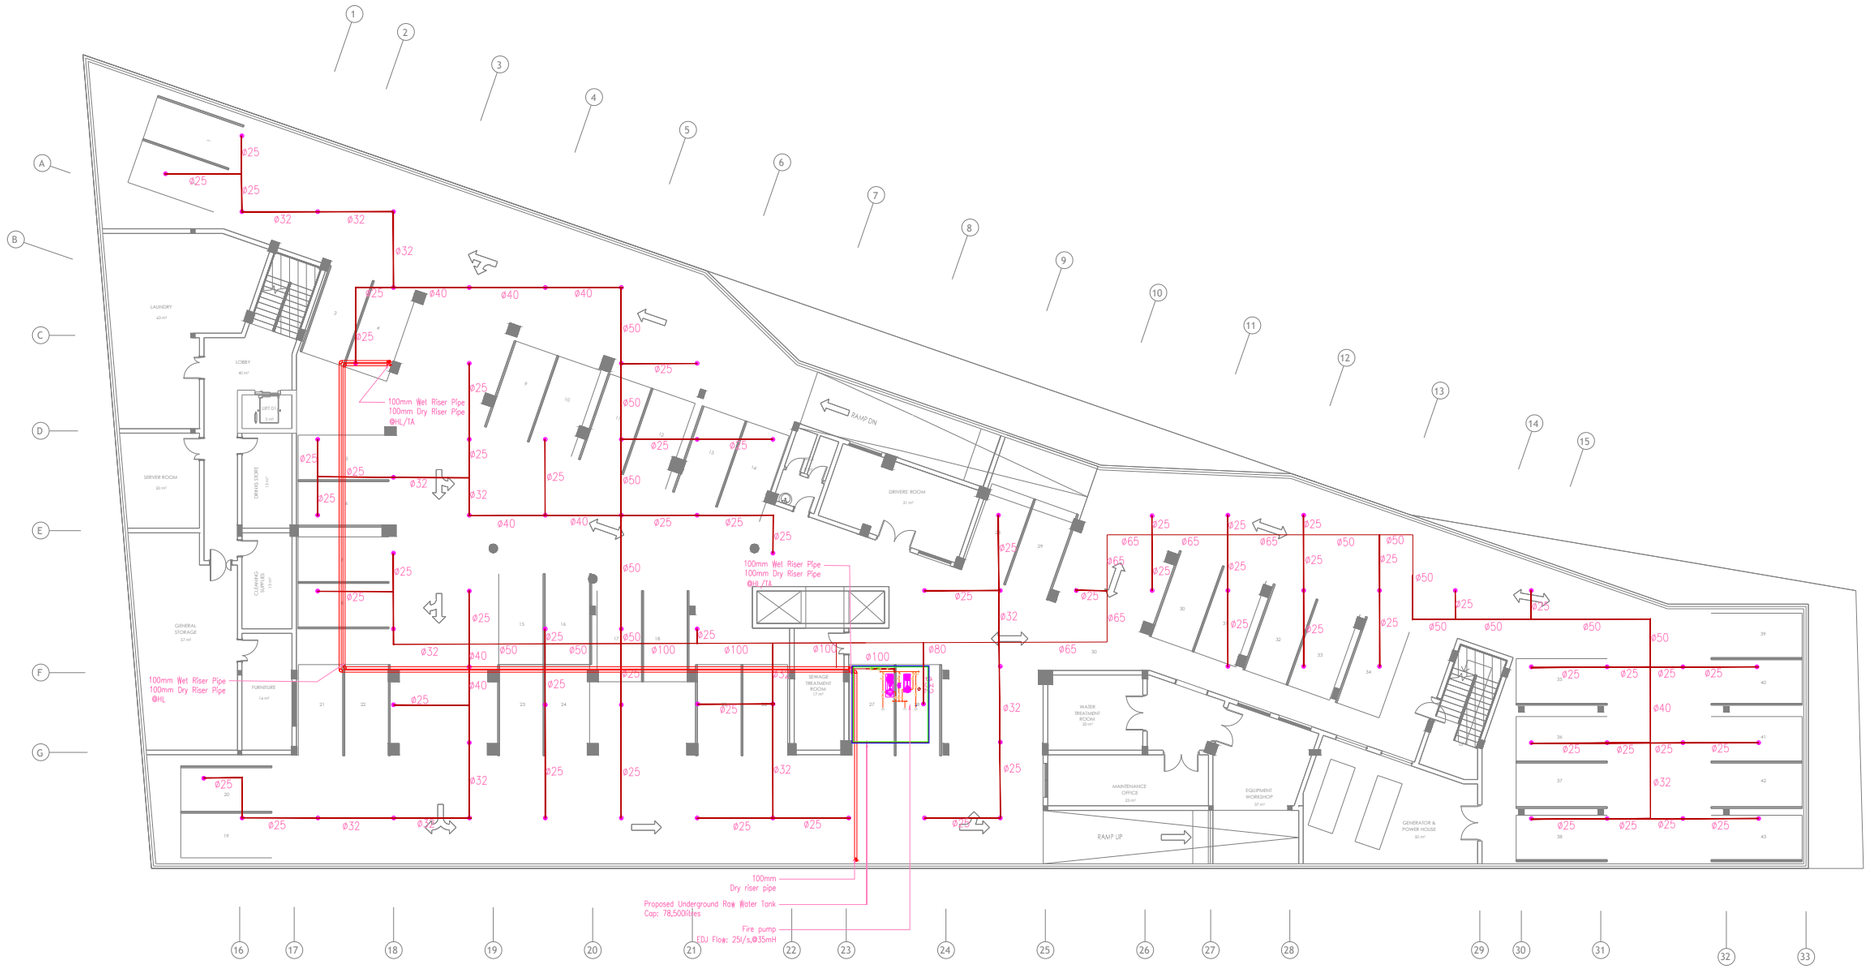

BASEMENT rev

BASEMENT PLAN FIREFIGHTING LAYOUT.

NOTES

-Measurements should be taken from c/c dimensions to be read, not scaled.

-Given dimensions in metric mm.

-Architectural drawing to be read in conjunction with relevant structural drawing.

-Any alteration to be done with the approval of the project architect.

Architects

CLIENT

KING GEORGE HOTEL IKEJA.

PROJECT TITLE


PROPOSED KING GEORGE COURT LUXURY HOTEL DEVELOPMENT.

SHEET TITLE

BASEMENT PLAN FIREFIGHTING LAYOUT

		DATE
DESIGNED BY	A.K	MAY,2026..
CAD BY	A.H	MAY,2026..
CHECKED BY		MAY,2026..

SCALE REF NO.	SHEET NO.		DRAWING NO.
			DR-01

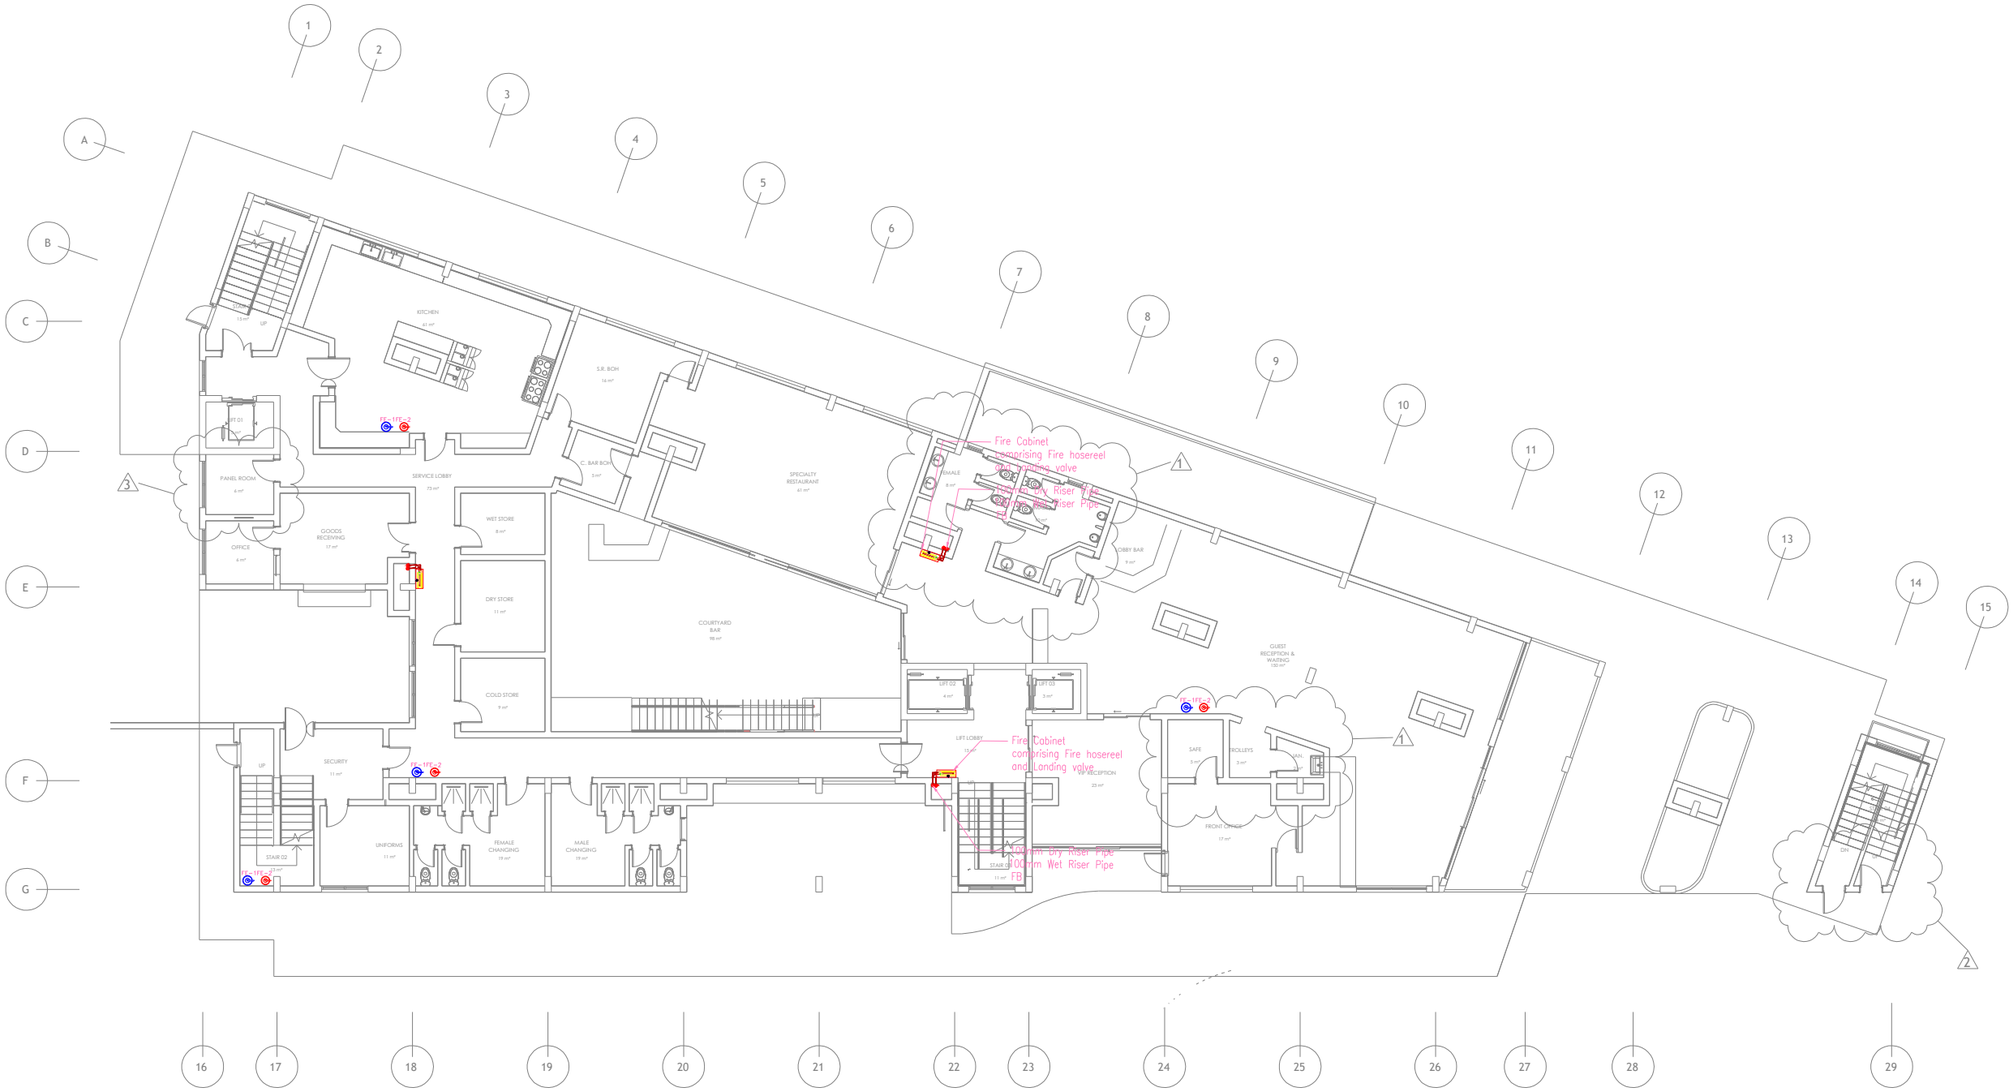

GROUND FLOOR PLAN FIREFIGHTING LAYOUT.

GROUND FLOOR rev

NOTES

-Measurements should be taken from c/c dimensions to be read, not scaled.

-Given dimensions in metric mm.

-Architectural drawing to be read in conjunction with relevant structural drawing.

-Any alteration to be done with the approval of the project architect.

Architects

CLIENT

KING GEORGE HOTEL IKEJA.

PROJECT TITLE


PROPOSED KING GEORGE COURT LUXURY HOTEL DEVELOPMENT.

SHEET TITLE

GROUND FLOOR PLAN FIREFIGHTING LAYOUT

		DATE
DESIGNED BY	A.K	MAY,2026..
CAD BY	A.H	MAY,2026..
CHECKED BY		MAY,2026..

SCALE REF NO.	SHEET NO.		DRAWING NO.
			DR-01

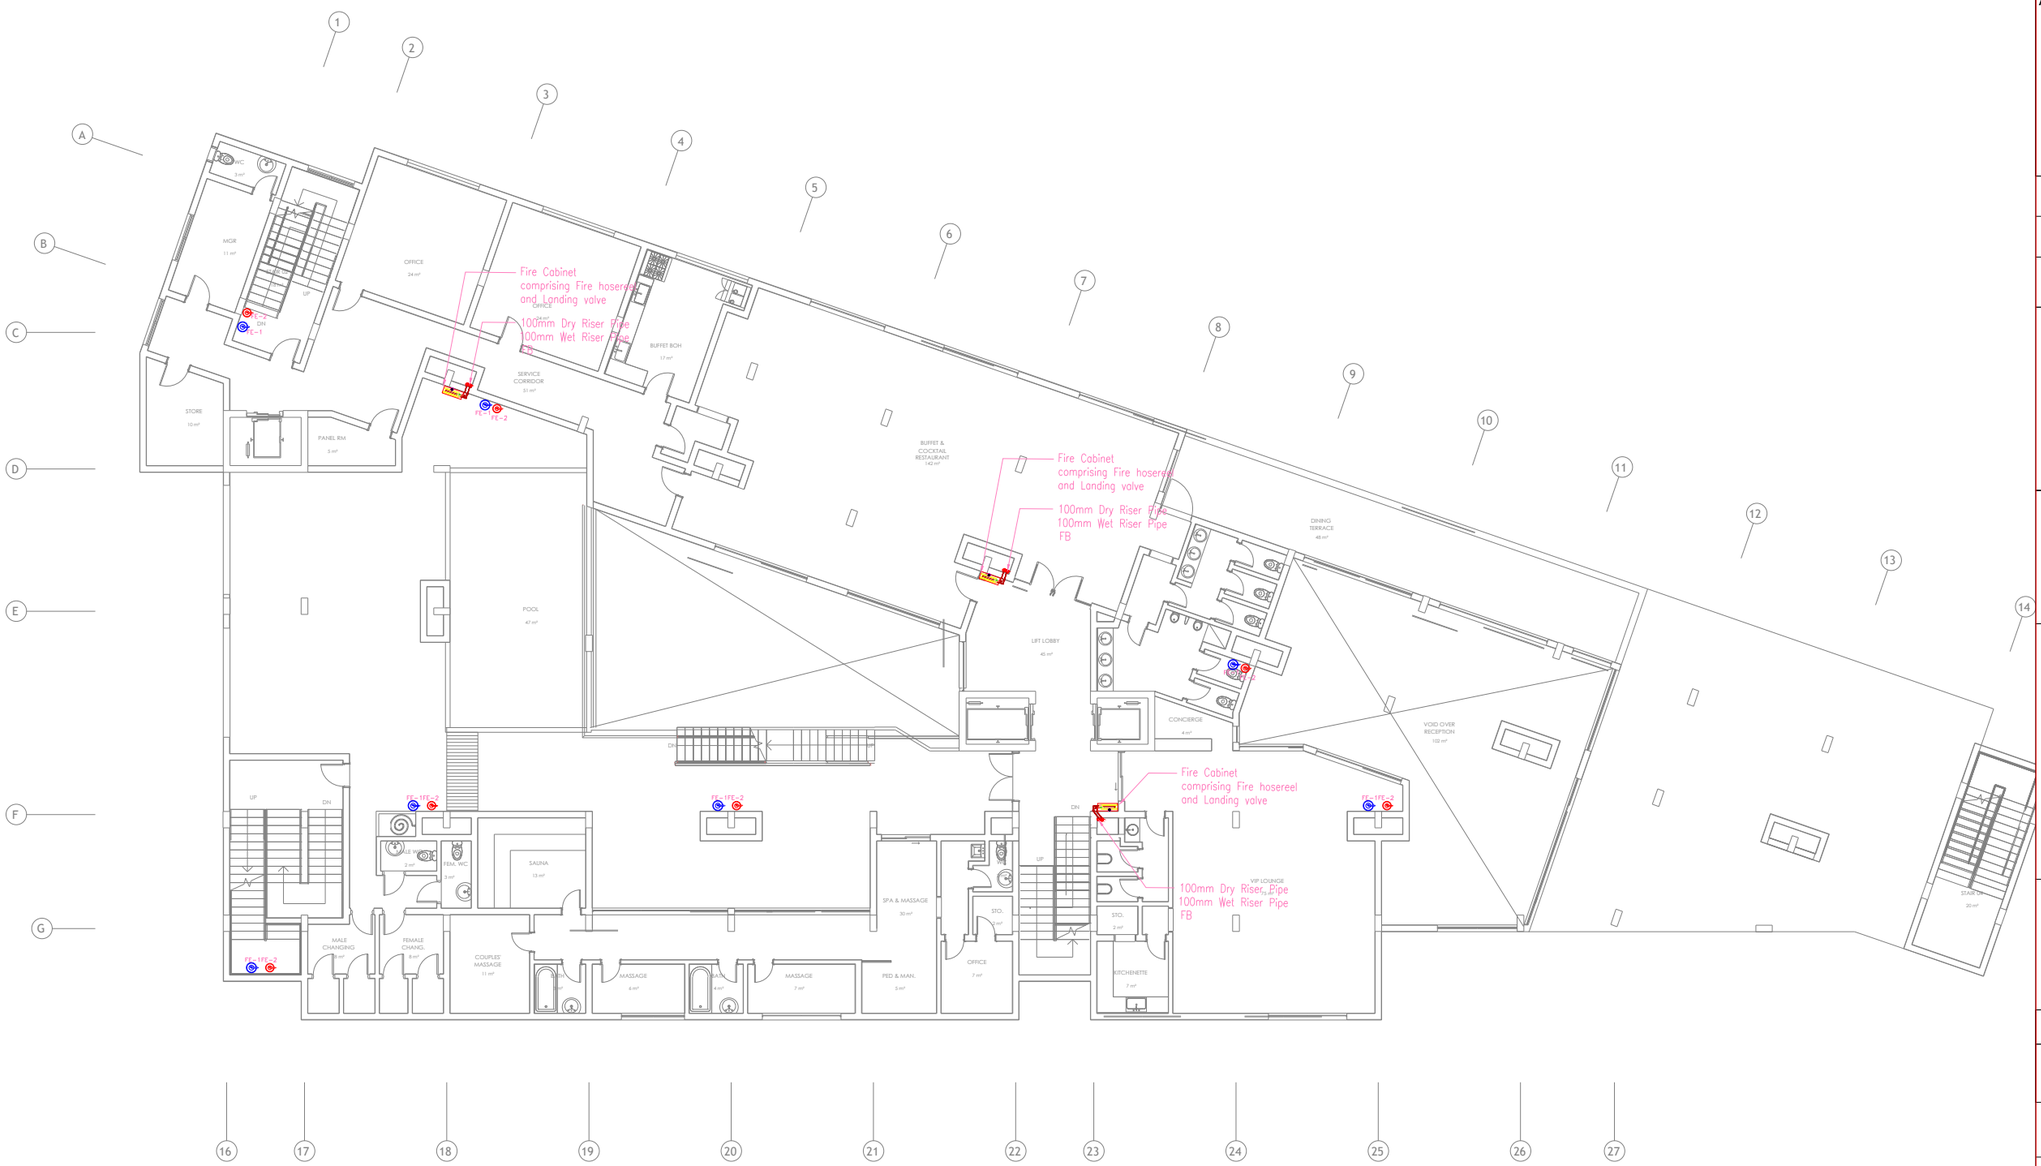

MEZZANINE FLOOR PLAN FIREFIGHTING LAYOUT.

MEZZ. rev

NOTES

-Measurements should be taken from c/c dimensions to be read, not scaled.

-Given dimensions in metric mm.

-Architectural drawing to be read in conjunction with relevant structural drawing.

-Any alteration to be done with the approval of the project architect.

Architects

CLIENT

KING GEORGE HOTEL IKEJA.

PROJECT TITLE


PROPOSED KING GEORGE COURT LUXURY HOTEL DEVELOPMENT.

SHEET TITLE

MEZZANINE PLAN FIREFIGHTING LAYOUT

		DATE
DESIGNED BY	A.K	MAY,2026..
CAD BY	A.H	MAY,2026..
CHECKED BY		MAY,2026..

SCALE REF NO.	SHEET NO.		DRAWING NO.
			DR-01

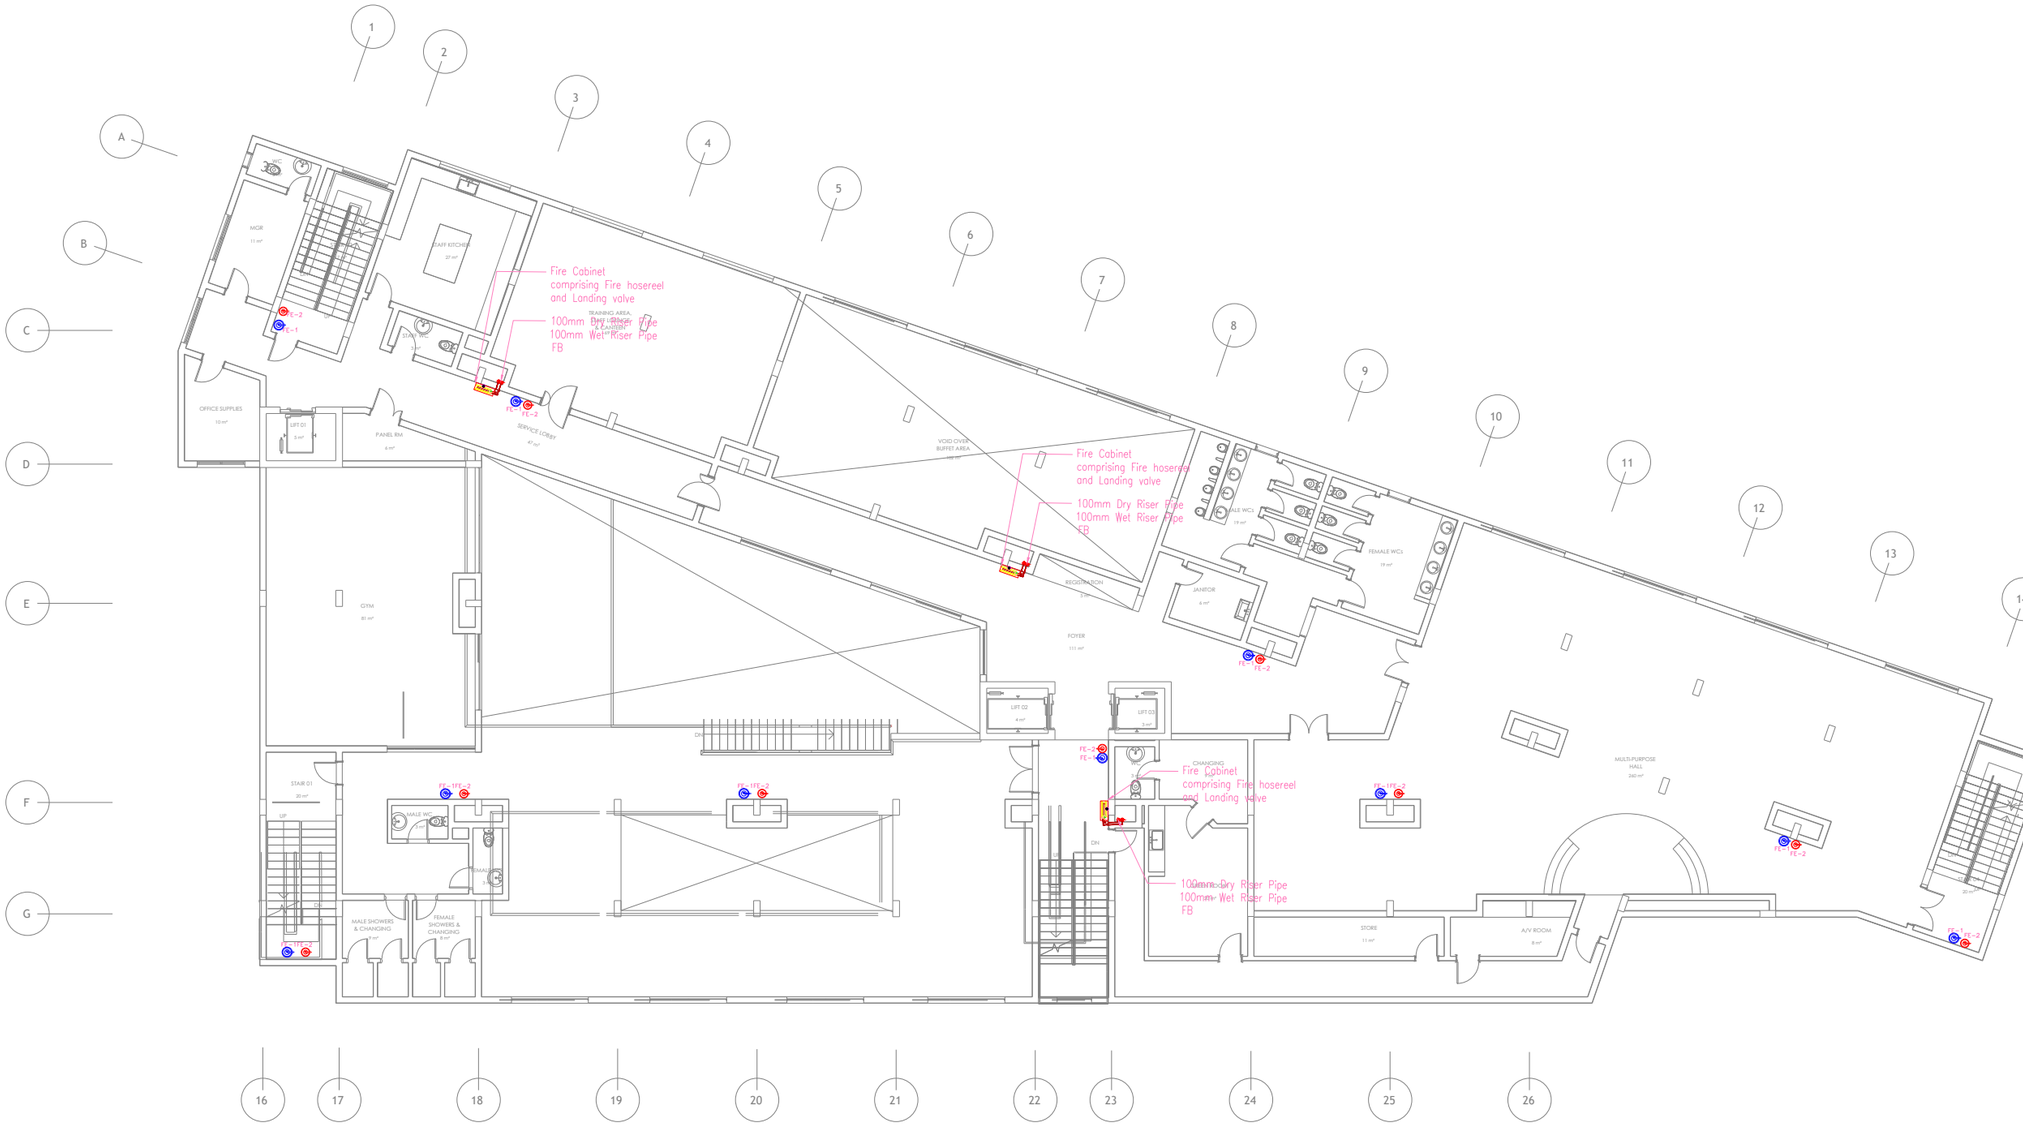

FIRST FLOOR PLAN
FIREFIGHTING LAYOUT.

1st Floor

NOTES

-Measurements should be taken from c/c dimensions to be read, not scaled.

-Given dimensions in metric mm.

-Architectural drawing to be read in conjunction with relevant structural drawing.

-Any alteration to be done with the approval of the project architect.

Architects

CLIENT

KING GEORGE HOTEL IKEJA.

PROJECT TITLE


PROPOSED KING GEORGE COURT LUXURY HOTEL DEVELOPMENT.

SHEET TITLE

FIRST FLOOR PLAN FIREFIGHTING LAYOUT

		DATE
DESIGNED BY	A.K	MAY,2026..
CAD BY	A.H	MAY,2026..
CHECKED BY		MAY,2026..

SCALE REF NO.	SHEET NO.		DRAWING NO.
			DR-01

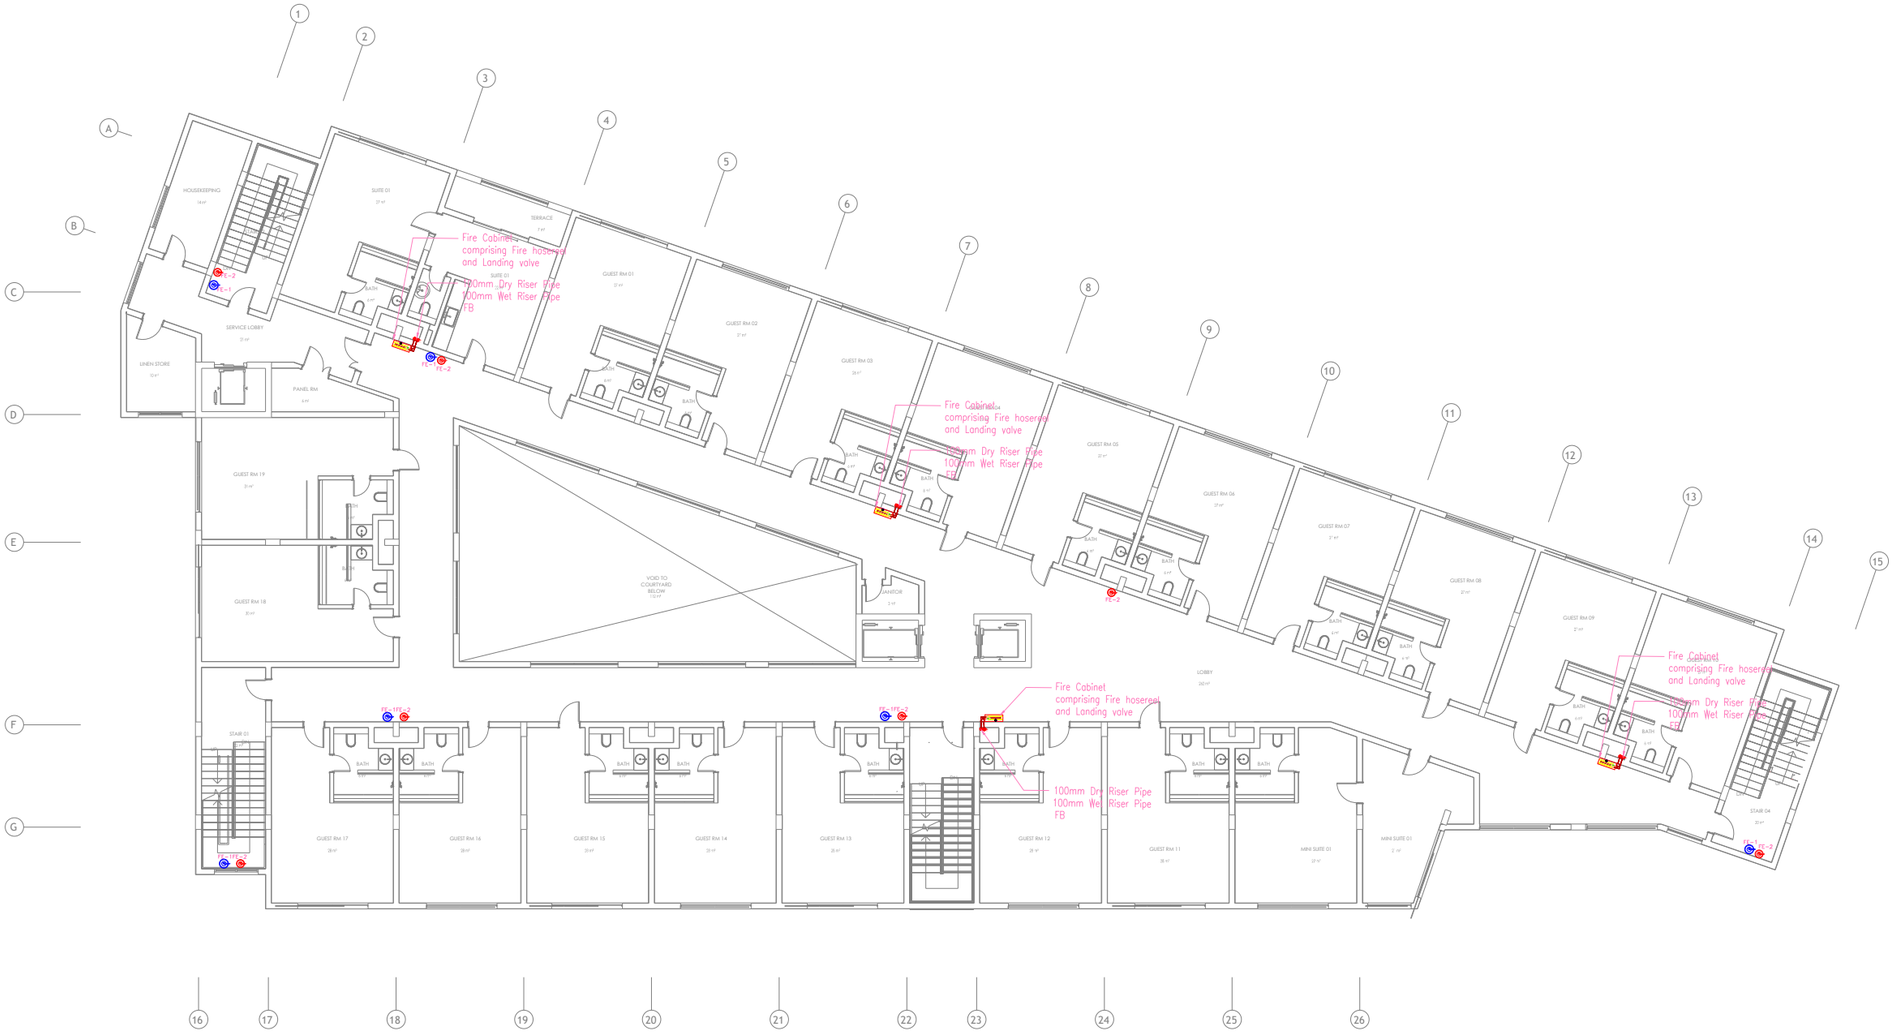

2,3&4 Floor...rev

2,3 & 4TH FLOOR PLAN FIREFIGHTING LAYOUT.

NOTES

-Measurements should be taken from c/
dimensions to be read, not scaled.

-Given dimensions in metric mm.

-Architectural drawing to be read in conjunction with relevant structural drawing.

-Any alteration to be done with the approval of the project architect.

Architects

CLIENT

KING GEORGE HOTEL IKEJA.

PROJECT TITLE


PROPOSED KING GEORGE COURT LUXURY HOTEL DEVELOPMENT.

SHEET TITLE

2,3 &4TH FLOOR PLAN FIREFIGHTING LAYOUT

		DATE
DESIGNED BY	A.K	MAY,2026..
CAD BY	A.H	MAY,2026..
CHECKED BY		MAY,2026..

SCALE REF NO.	SHEET NO.		DRAWING NO.
			DR-01

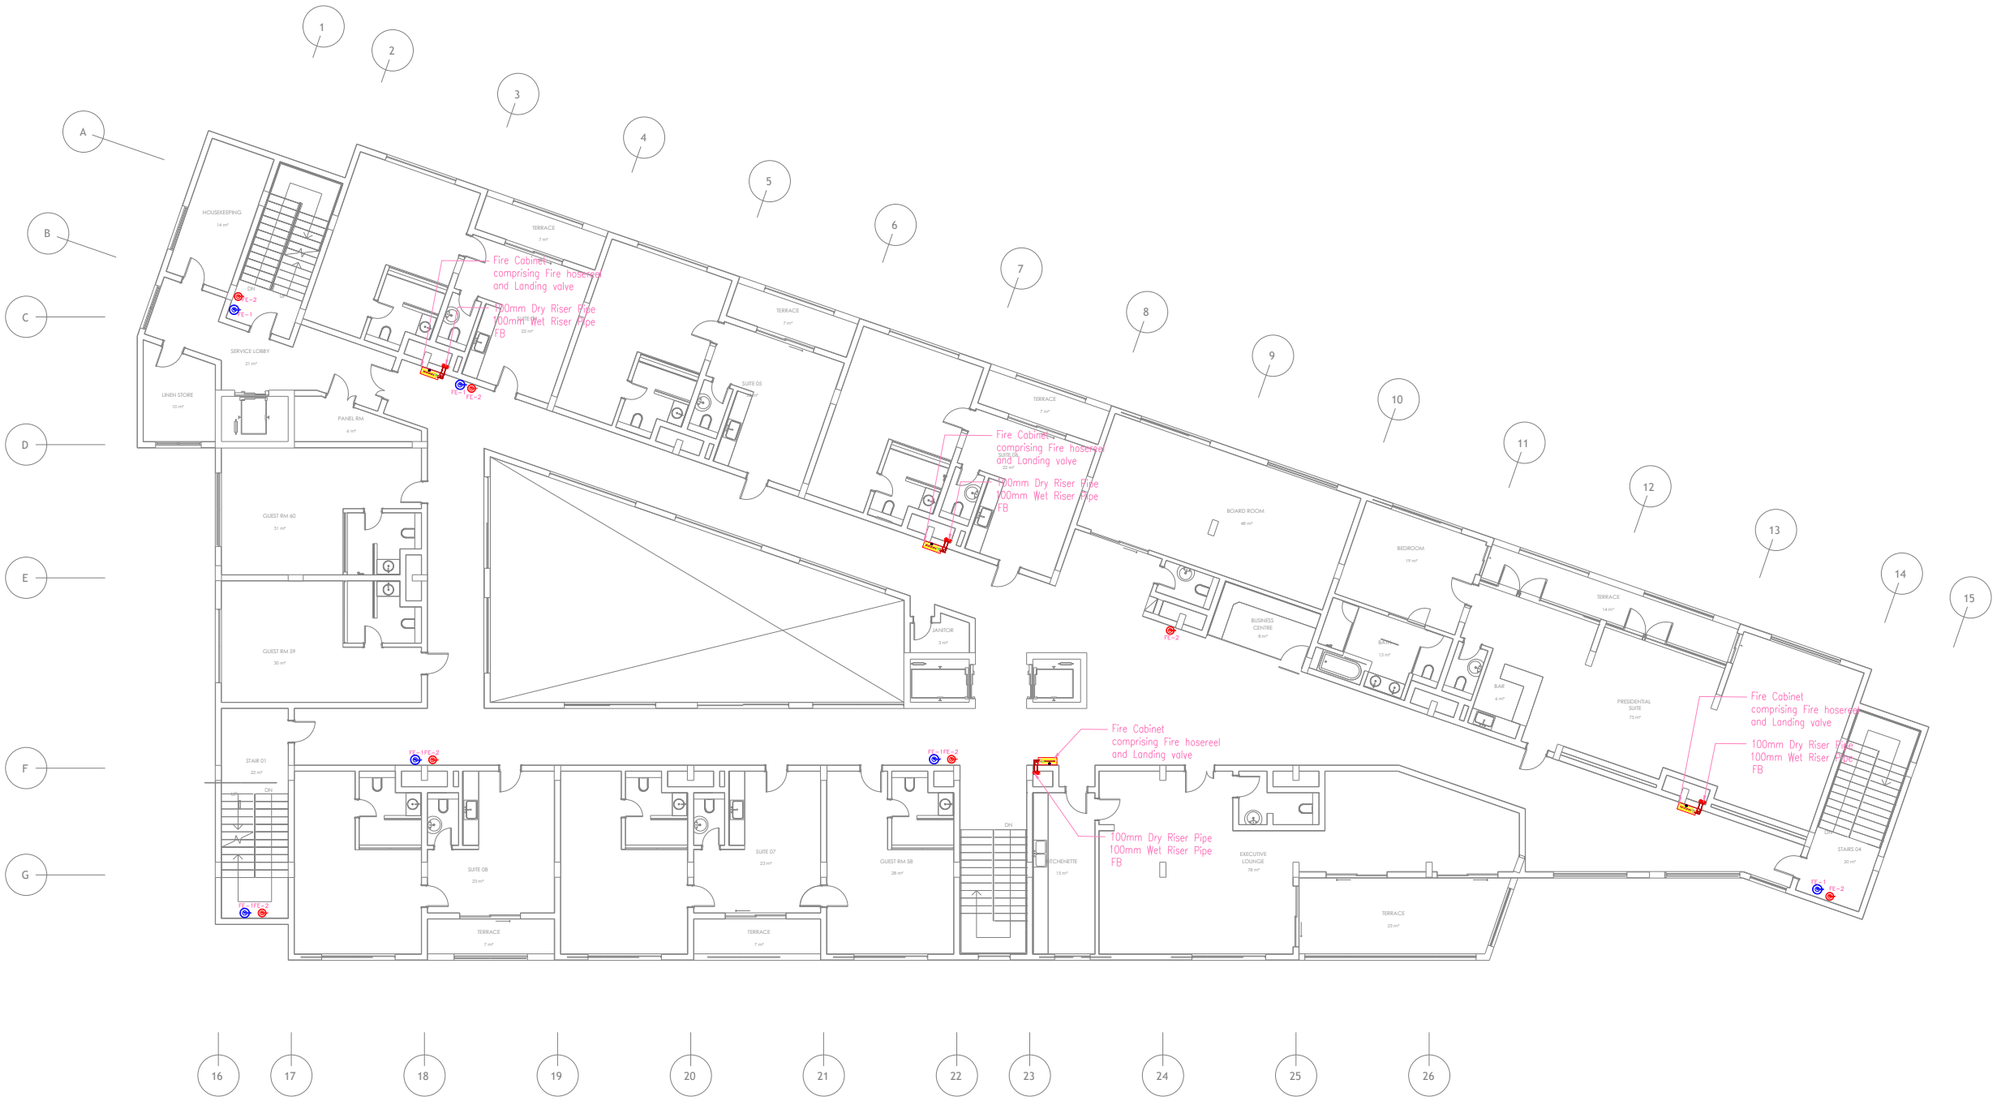

Pent Floor rev.

PENT FLOOR PLAN
FIREFIGHTING LAYOUT.

NOTES

-Measurements should be taken from c/c dimensions to be read, not scaled.

-Given dimensions in metric mm.

-Architectural drawing to be read in conjunction with relevant structural drawing.

-Any alteration to be done with the approval of the project architect.

Architects

CLIENT

KING GEORGE HOTEL IKEJA.

PROJECT TITLE

PROPOSED KING GEORGE COURT LUXURY HOTEL DEVELOPMENT.

SHEET TITLE

PENT FLOOR PLAN FIREFIGHTING LAYOUT

		DATE
DESIGNED BY	A.K	MAY,2026..
CAD BY	A.H	MAY,2026..
CHECKED BY		MAY,2026..

SCALE REF NO.	SHEET NO.		DRAWING NO.
			DR-01